


TIE-IN POINTS				
TIE-IN	SERVICE	NPS	CONN. TYPE	CLASS
TP-01	FEED (INLET)	3"	RF FLANGE	150 LB
TP-02	FILTER DRAIN	1/2"	NPT	
TP-03	EXHAUST	6"	RF FLANGE	150 LB


BILL OF MATERIAL			
ITEM	QTY	DESCRIPTION	PART NO.
1	1	G4 VALVE HIGHER PURITY & SUPPORT ASSEMBLY (G4-P-ASME)	A1213725
2	9	PSA VESSEL ASSEMBLY	A1213695
3	1	TOP SPIDER ASSEMBLY PSA30-90H-G4-250A-120-SP	A1213727
4	1	BOTTOM SPIDER ASSEMBLY PSA30-90H-G4-250A-120-SP	A1213729
5	1	FEED PIPING ASSEMBLY PSA30-90H-G4-250A-120-SP	A1213731
6	1	PRODUCT PIPING ASSEMBLY PSA30-90H-G4-250A-120-SP	A1213733
7	1	EXHAUST PIPING ASSEMBLY PSA30-90H-G4-250A-120-SP	A1213735
8	1	SKID FOR PSA30-90H-G4-250A-120-SP	P1213737
9	4	BOLTING LIFTING LUG ASSEMBLY	A106951
10	1	PIPE SUPPORT ASSEMBLY	A1213835
11	1	PIPE SUPPORT ASSEMBLY	A1213836
12	1	PIPE SUPPORT ASSEMBLY	A1213837
13	1	PIPE SUPPORT ASSEMBLY	A1213838
14	1	PIPE SUPPORT ASSEMBLY	A1213839

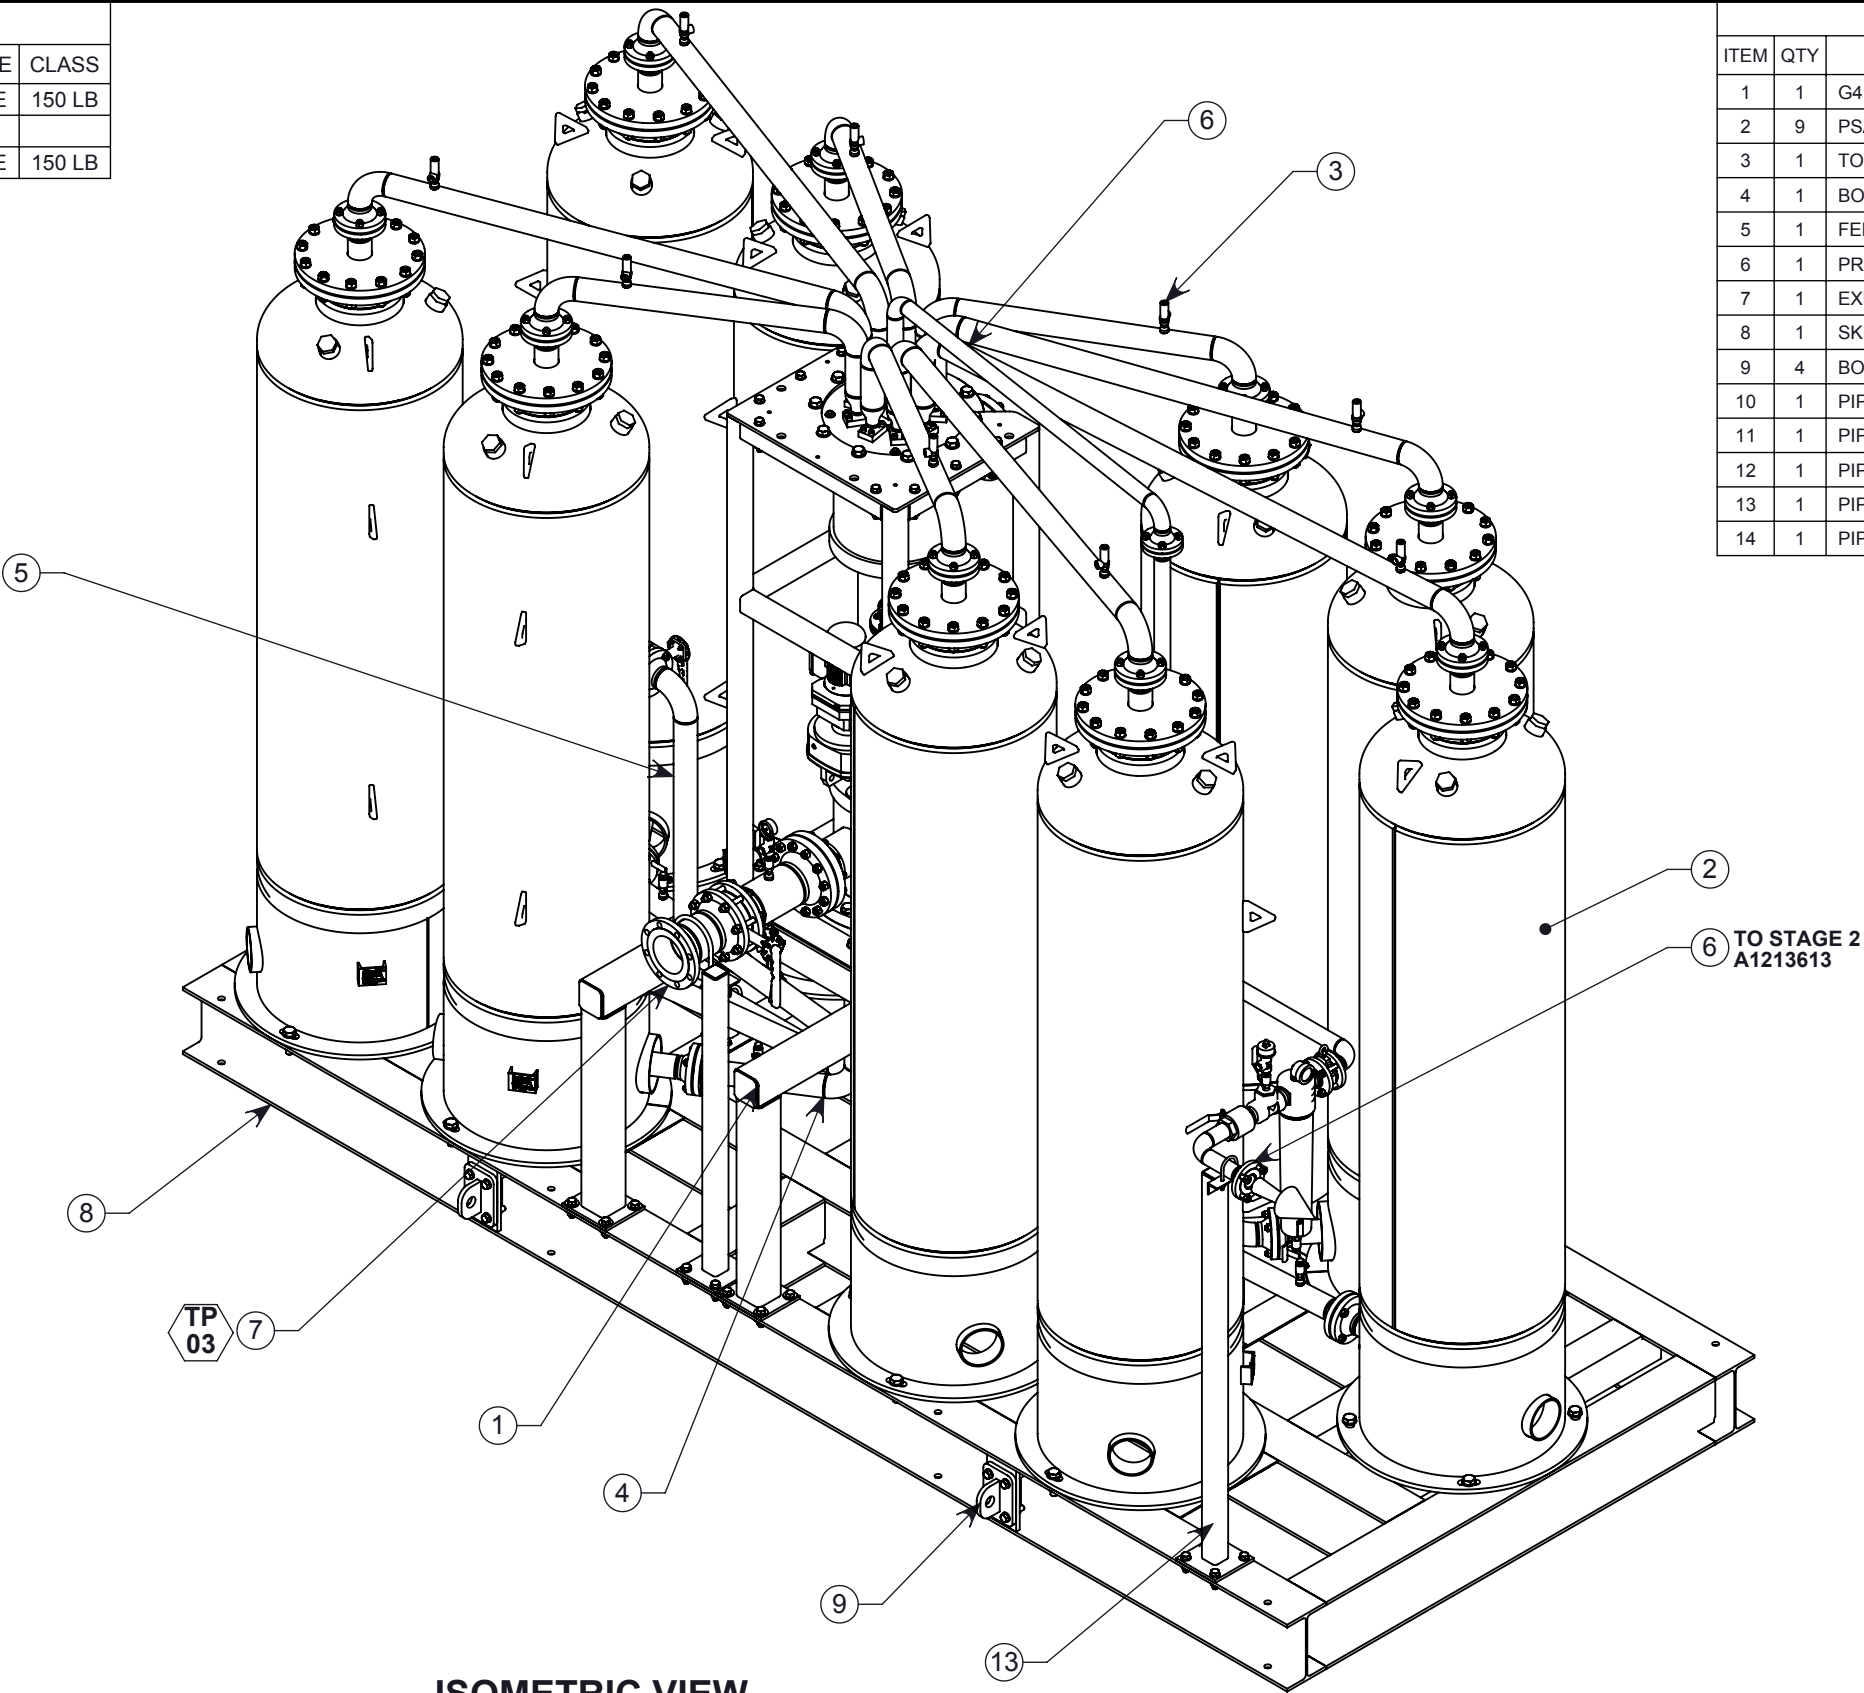

ISOMETRIC VIEW
(FRONT)

- NOTES:
- 1. TOTAL PRELIMINARY ESTIMATED WEIGHT:
 - EMPTY VESSELS: **35000** lbs.
 - WITH DESICCANT: **49400** lbs.
 - 2. SEE P&ID **Y1213667** FOR REFERENCE.
 - 3. MINIMUM MAINTENANCE CLEARANCE REQUIRED.

xebec 730 Bpnl. INDUSTRIEL, BLAINVILLE, QUÉBEC, J7C 3V4 (CANADA) Tel.: (450) 979-8700 Fax.: (450) 979-7869	</
---	--	--	----

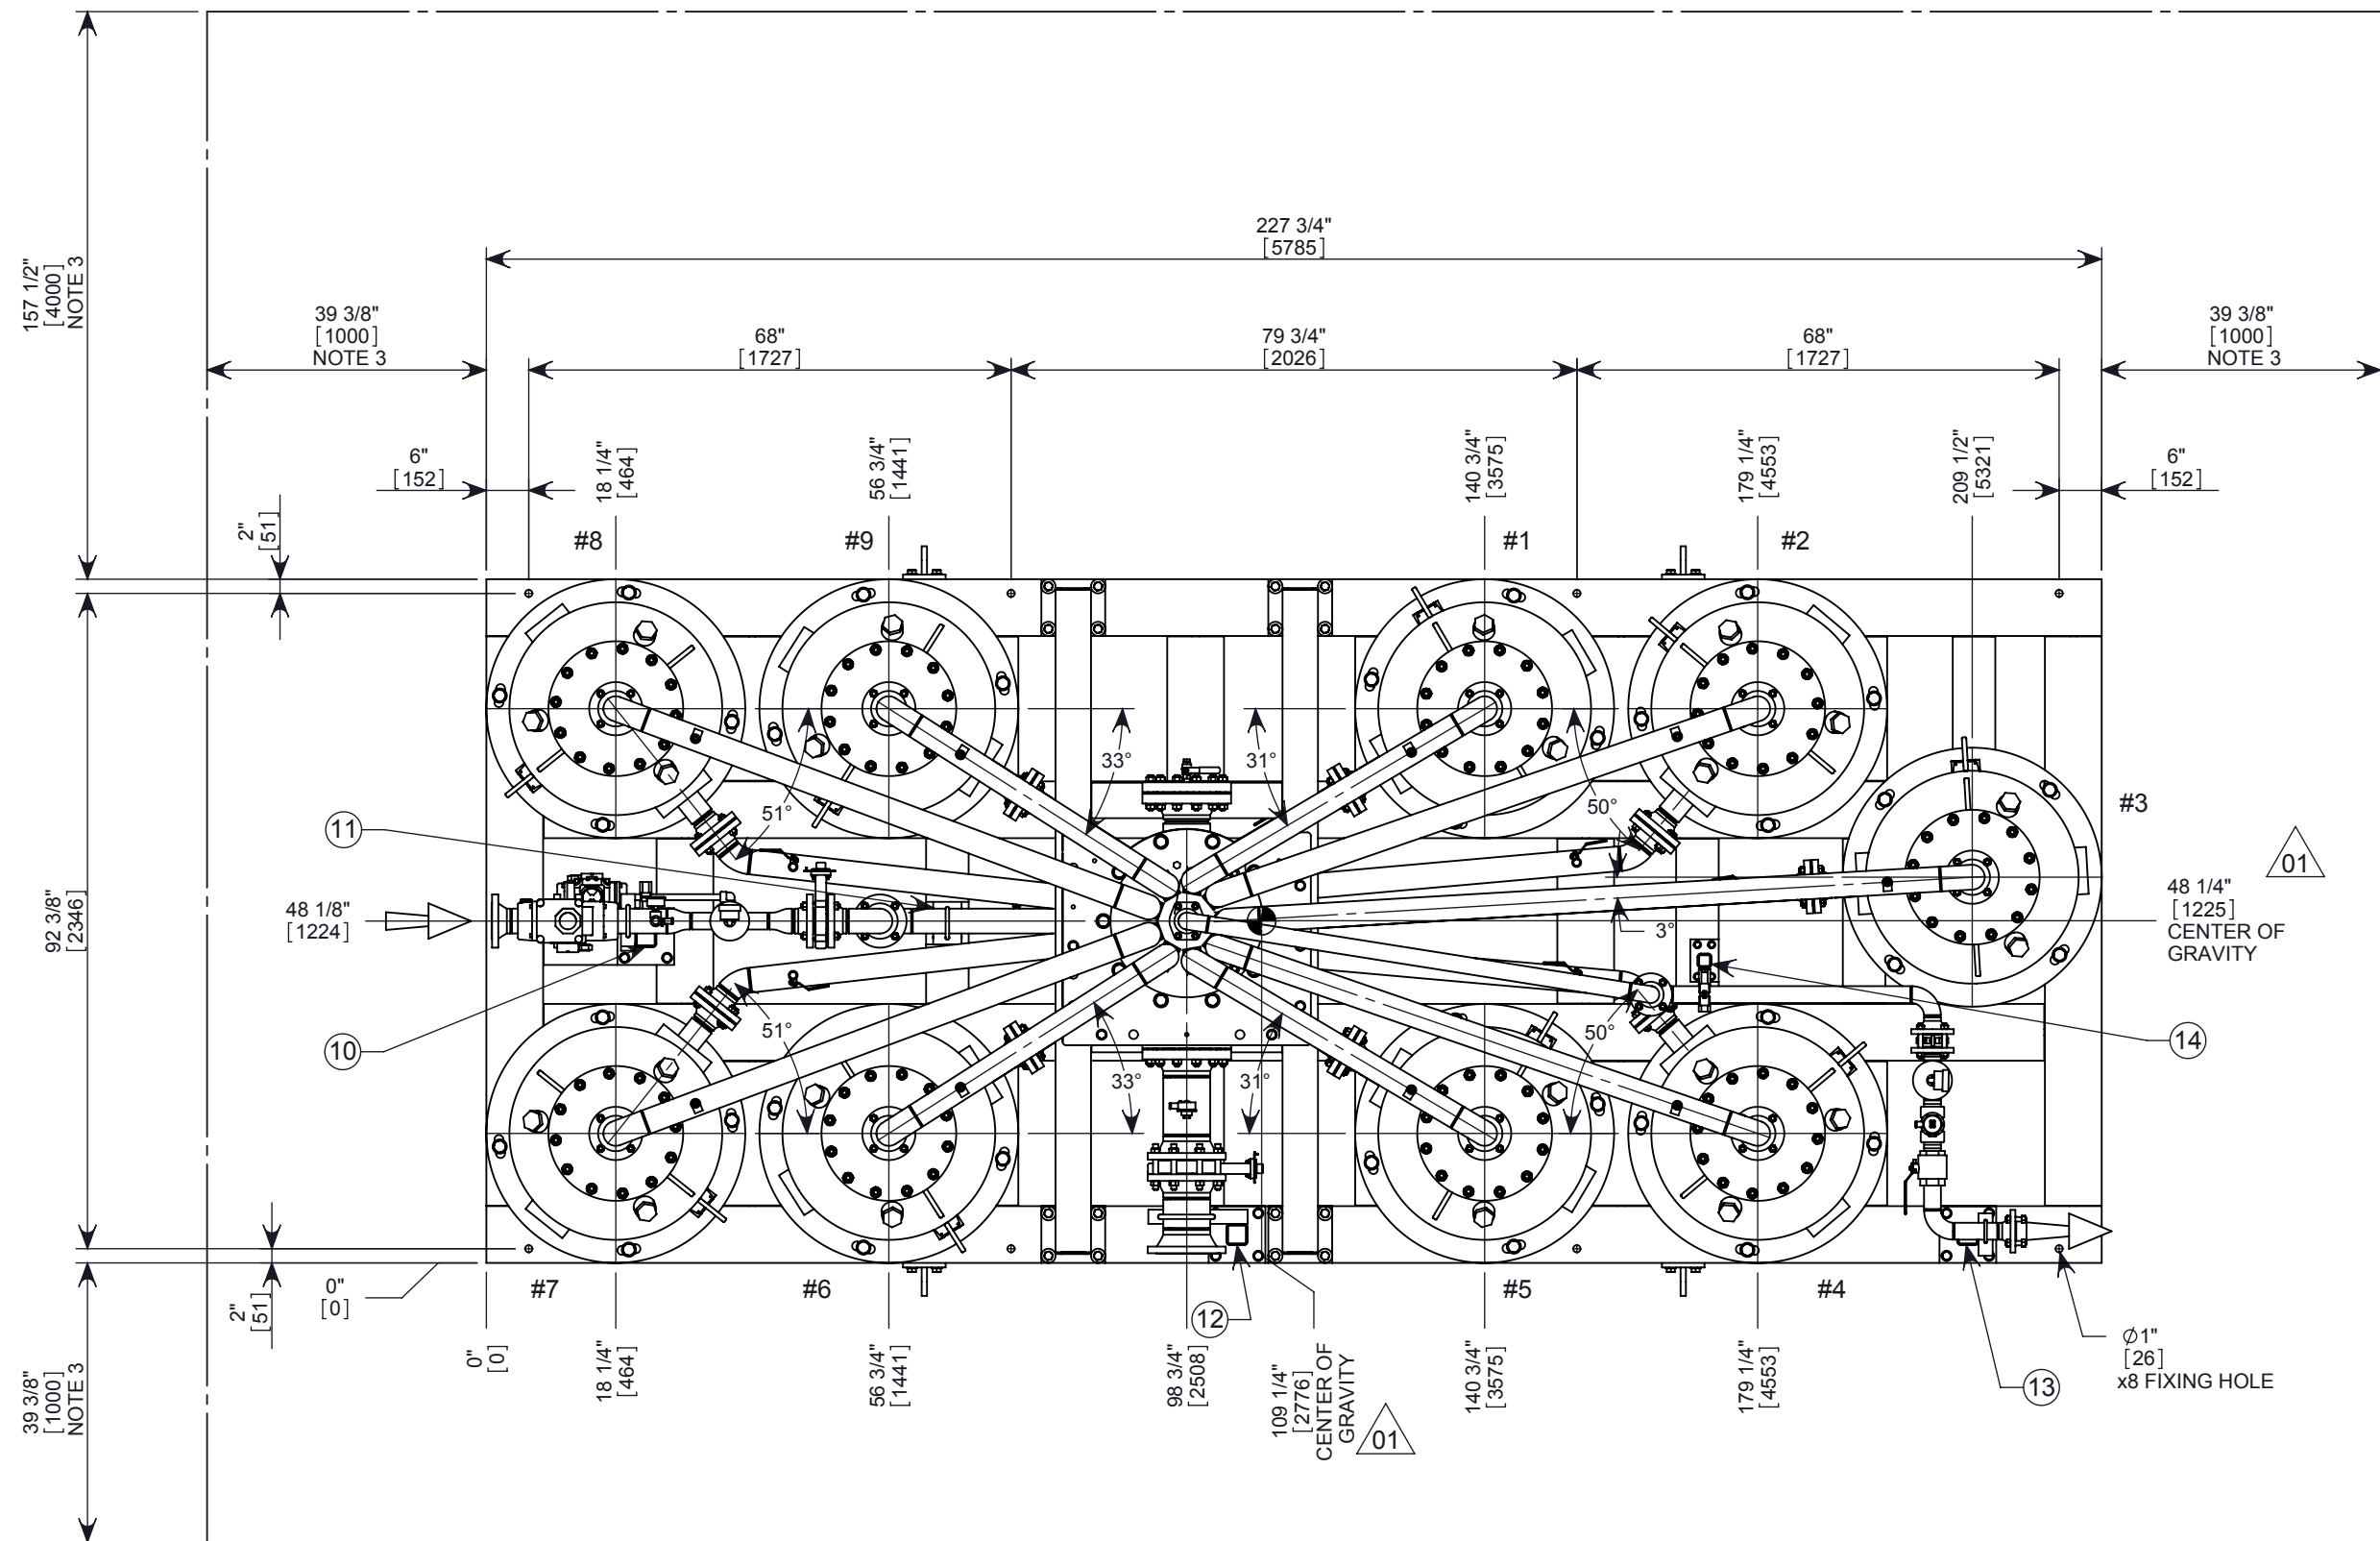


TOP VIEW


xebec
730 Boul. INDUSTRIEL, BLAINVILLE,
QUÉBEC, J7C 3V4 (CANADA)
Tel.: (450) 979-8700
Fax.: (450) 979-7869

THE ORIGINAL OF THIS DRAWING IS COPYRIGHT AND
CONTAINS CONFIDENTIAL INFORMATION. IT IS THE
PROPERTY OF XEBEC INC. WITHOUT WHOSE PERMISSION IT
MAY NOT BE COPIED, SHOWN OR HANDED TO A THIRD
PARTY OR OTHERWISE USED AND IT IS TO BE RETURNED
PROMPTLY UPON REQUEST TO XEBEC INC.

TOLERANCE (INCHES):							
GENERALE: .XX: ±0.12"							
.XXX: ±0.063"							
X/X: ±1/32"							
ANGLE: ±1/2°							
(EXCEPT CHAMFER)							
THIRD ANGLE PROJECTION:							

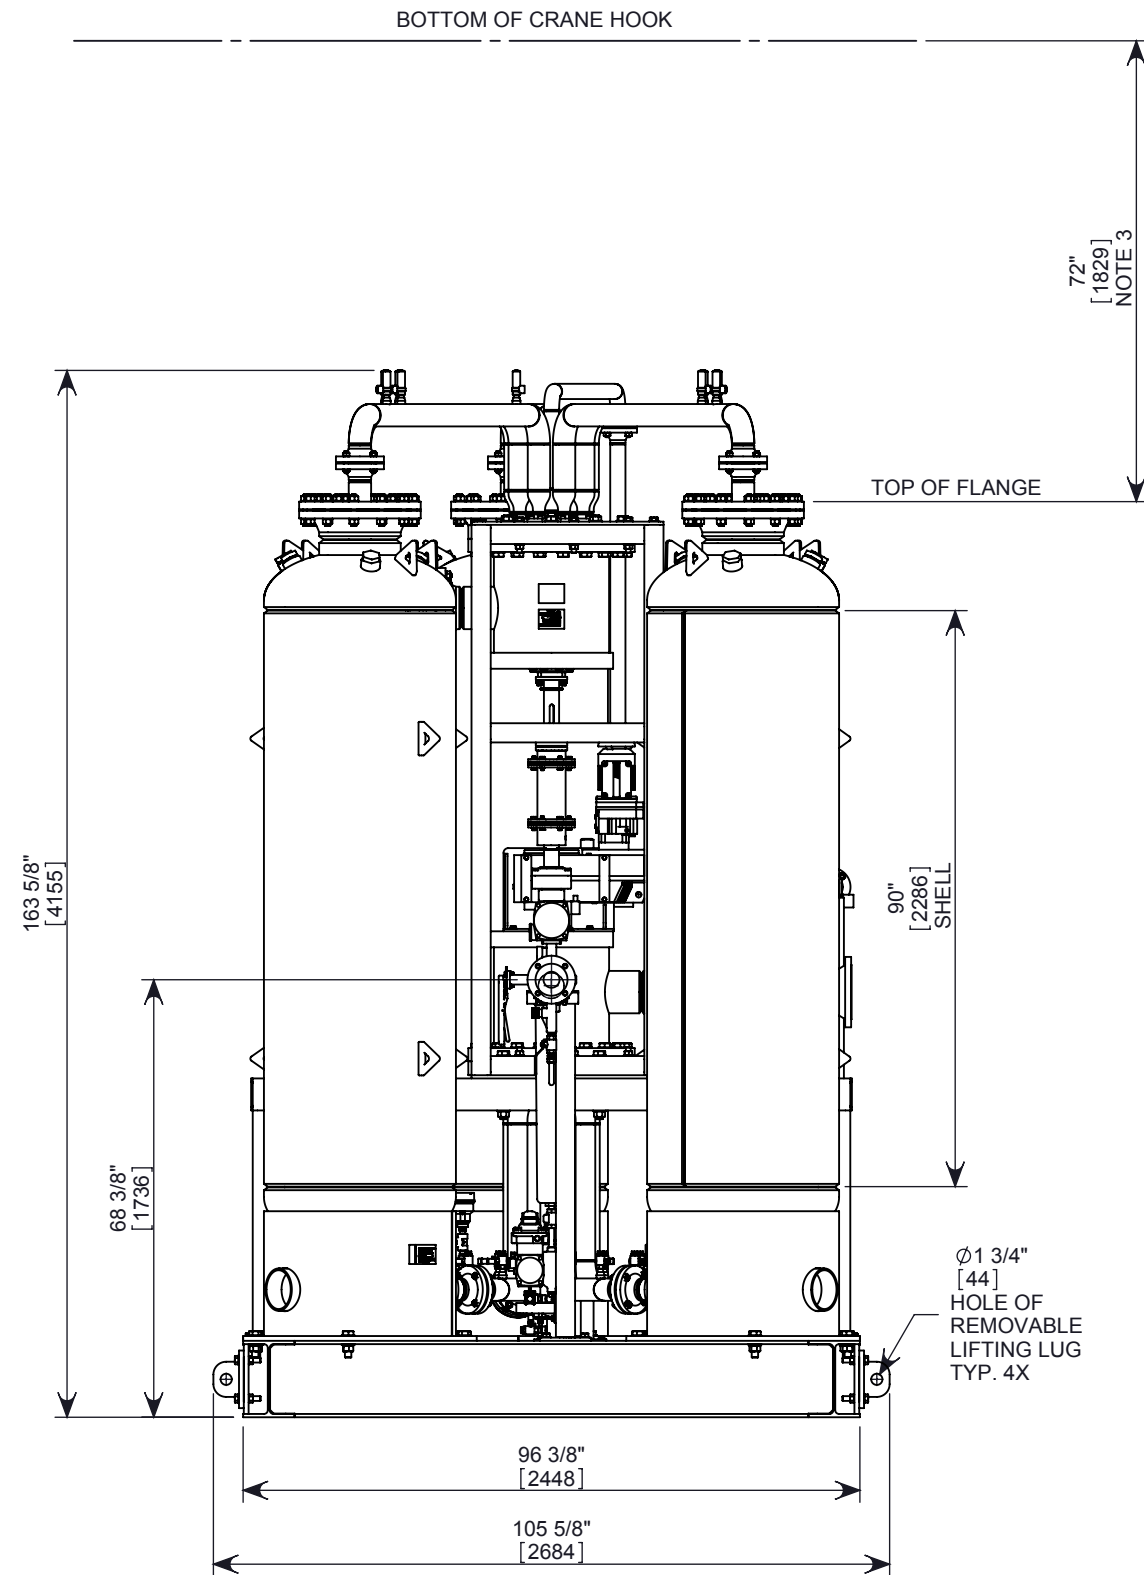

SIDE VIEW

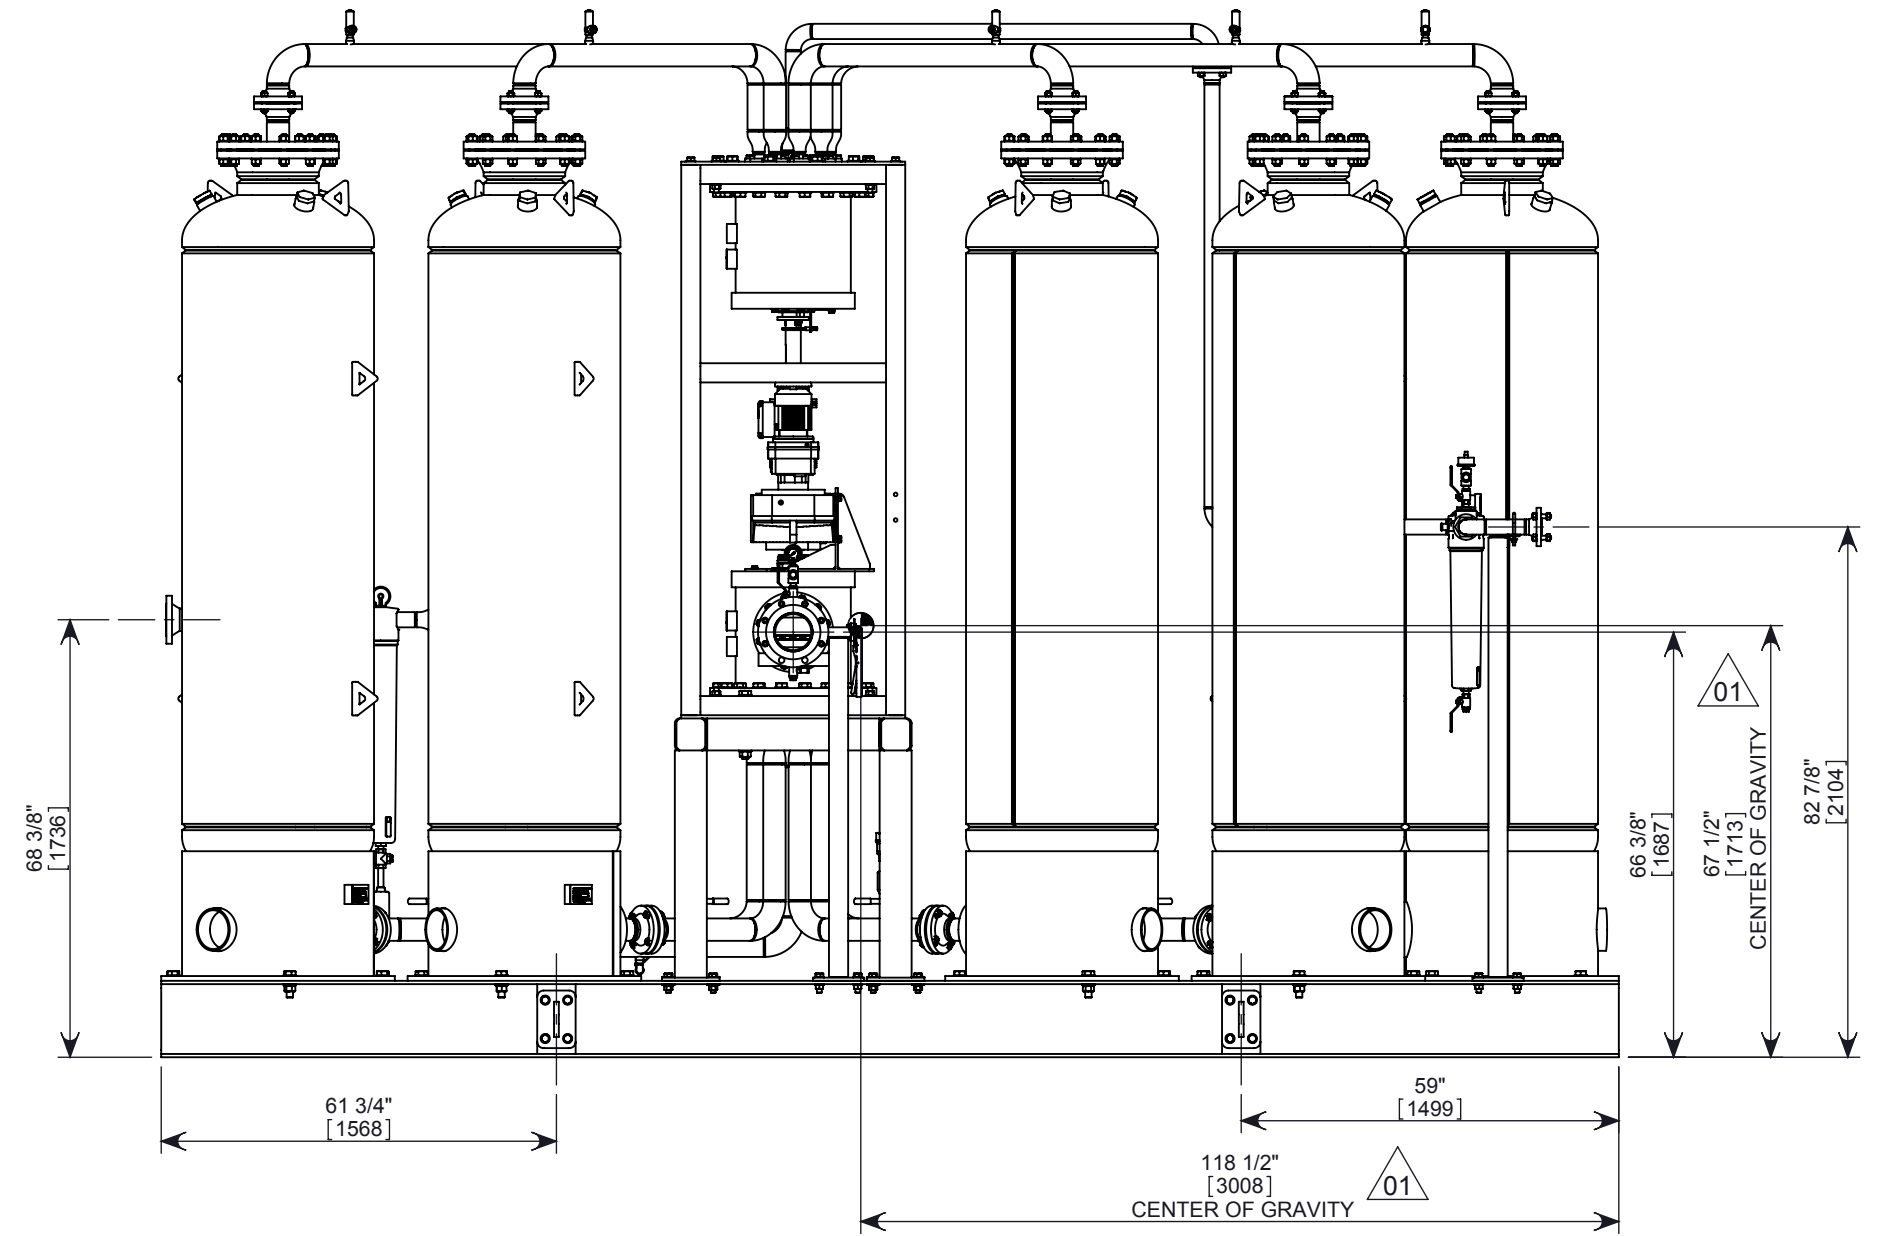

FRONT VIEW

xebec 730 Boul. INDUSTRIEL, BLAINVILLE, QUÉBEC, J7C 3V4 (CANADA) Tel.: (450) 979-8700 Fax.: (450) 979-7869				TOLERANCE (INCHES):			
				GENERALE: .XX: ±0.12" .XXX: ±0.063" X/X: ±1/32" ANGLE: ±1/2° (EXCEPT CHAMFER)			
01 CENTER OF GRAVITY ADDED				2020-02-06	VTA	PMO	GSA
00 FIRST ISSUE				2019-06-18	VTA	PMO	GSA
REV.	DESCRIPTION			DATE	DSS	CHK	APP.
	DRAWN	CHECKED	APPROVED	TITLE: PSA30-90H-G4-250A-120-SP			
NAME :	VTA	PMO	GSA	GENERAL ARRANGEMENT (STAGE 1)			
DATE :	2019-06-14	2019-06-18	2019-06-18	FORMAT:	DWG NO. :		PAGE:
				B	A1213612		4 de 4